PARTICION MATERIAL DE LOS HEREDEROS
DEL PREDIO DE FERMIN SUAREZ
UBICADO EN EL CORREGIMIENTO
DE EL ARENILLO
MUNICIPIO PALMIRA "VALLE"

[illegible] DE CADA LOTE

L. 1 {
NORTE: LUZ DE BEJARANO
SUR: RIO AGUA CLARA
ORIENTE: CARMELINA SUAREZ Y FRANOR ALVAREZ
OCCIDENTE: LUZ DE BEJARANO Y RIO AGUA CLARA

L. 2 {
NORTE: LUZ DE BEJARANO
SUR: FRANOR SUAREZ
ORIENTE: LAURENTINO SUAREZ
OCCIDENTE: PAULINA SUAREZ

L. 3 {
NORTE: LAURENTINO Y CARMELINA SUAREZ
SUR: FRANOR ALVAREZ
ORIENTE: WENCESLAO LOPEZ
OCCIDENTE: PAULINA SUAREZ

L. 4 Laurentino Suarez {
NORTE: LUZ DE BEJARANO
SUR: FRANOR ALVAREZ
ORIENTE: ~~LUCIA SUAREZ~~ Y RICARDO LOPEZ
OCCIDENTE: CARMELINA SUAREZ

L. 5 Lucia Suarez {
NORTE: LUZ DE BEJARANO
SUR: RICARDO LOPEZ
ORIENTE: SERGIO PEPICANO
OCCIDENTE: LAURENTINO SUAREZ

L. 6 Sergio Pepicano {
NORTE: LUZ DE BEJARANO
SUR: RICARDO LOPEZ
ORIENTE: PAULINA SUAREZ
OCCIDENTE: LUZ DE BEJARANO

L. 7 Paulina Suarez {
NORTE: SERGIO PEPICANO
SUR: RICARDO LOPEZ
ORIENTE: JOSE EVANGELISTA ARBOLEDA
OCCIDENTE: SERGIO PEPICANO

L. 8 Sergio Pepicano {
NORTE: LUZ DE BEJARANO Y GONZALO SARRIA
SUR: PAULINA SUAREZ
ORIENTE: GONZALO SARRIA Y JOSE LINO ARBOLEDA
OCCIDENTE: LUZ DE BEJARANO

AREA TOTAL DEL PREDIO
16 PLAZAS Y 423 MTS²

E. 1:2.000

LV. DB. Y CALC.

[illegible] Pj.

Jaime Lopez S.
[illegible] Palmira

[illegible] 15 [illegible]

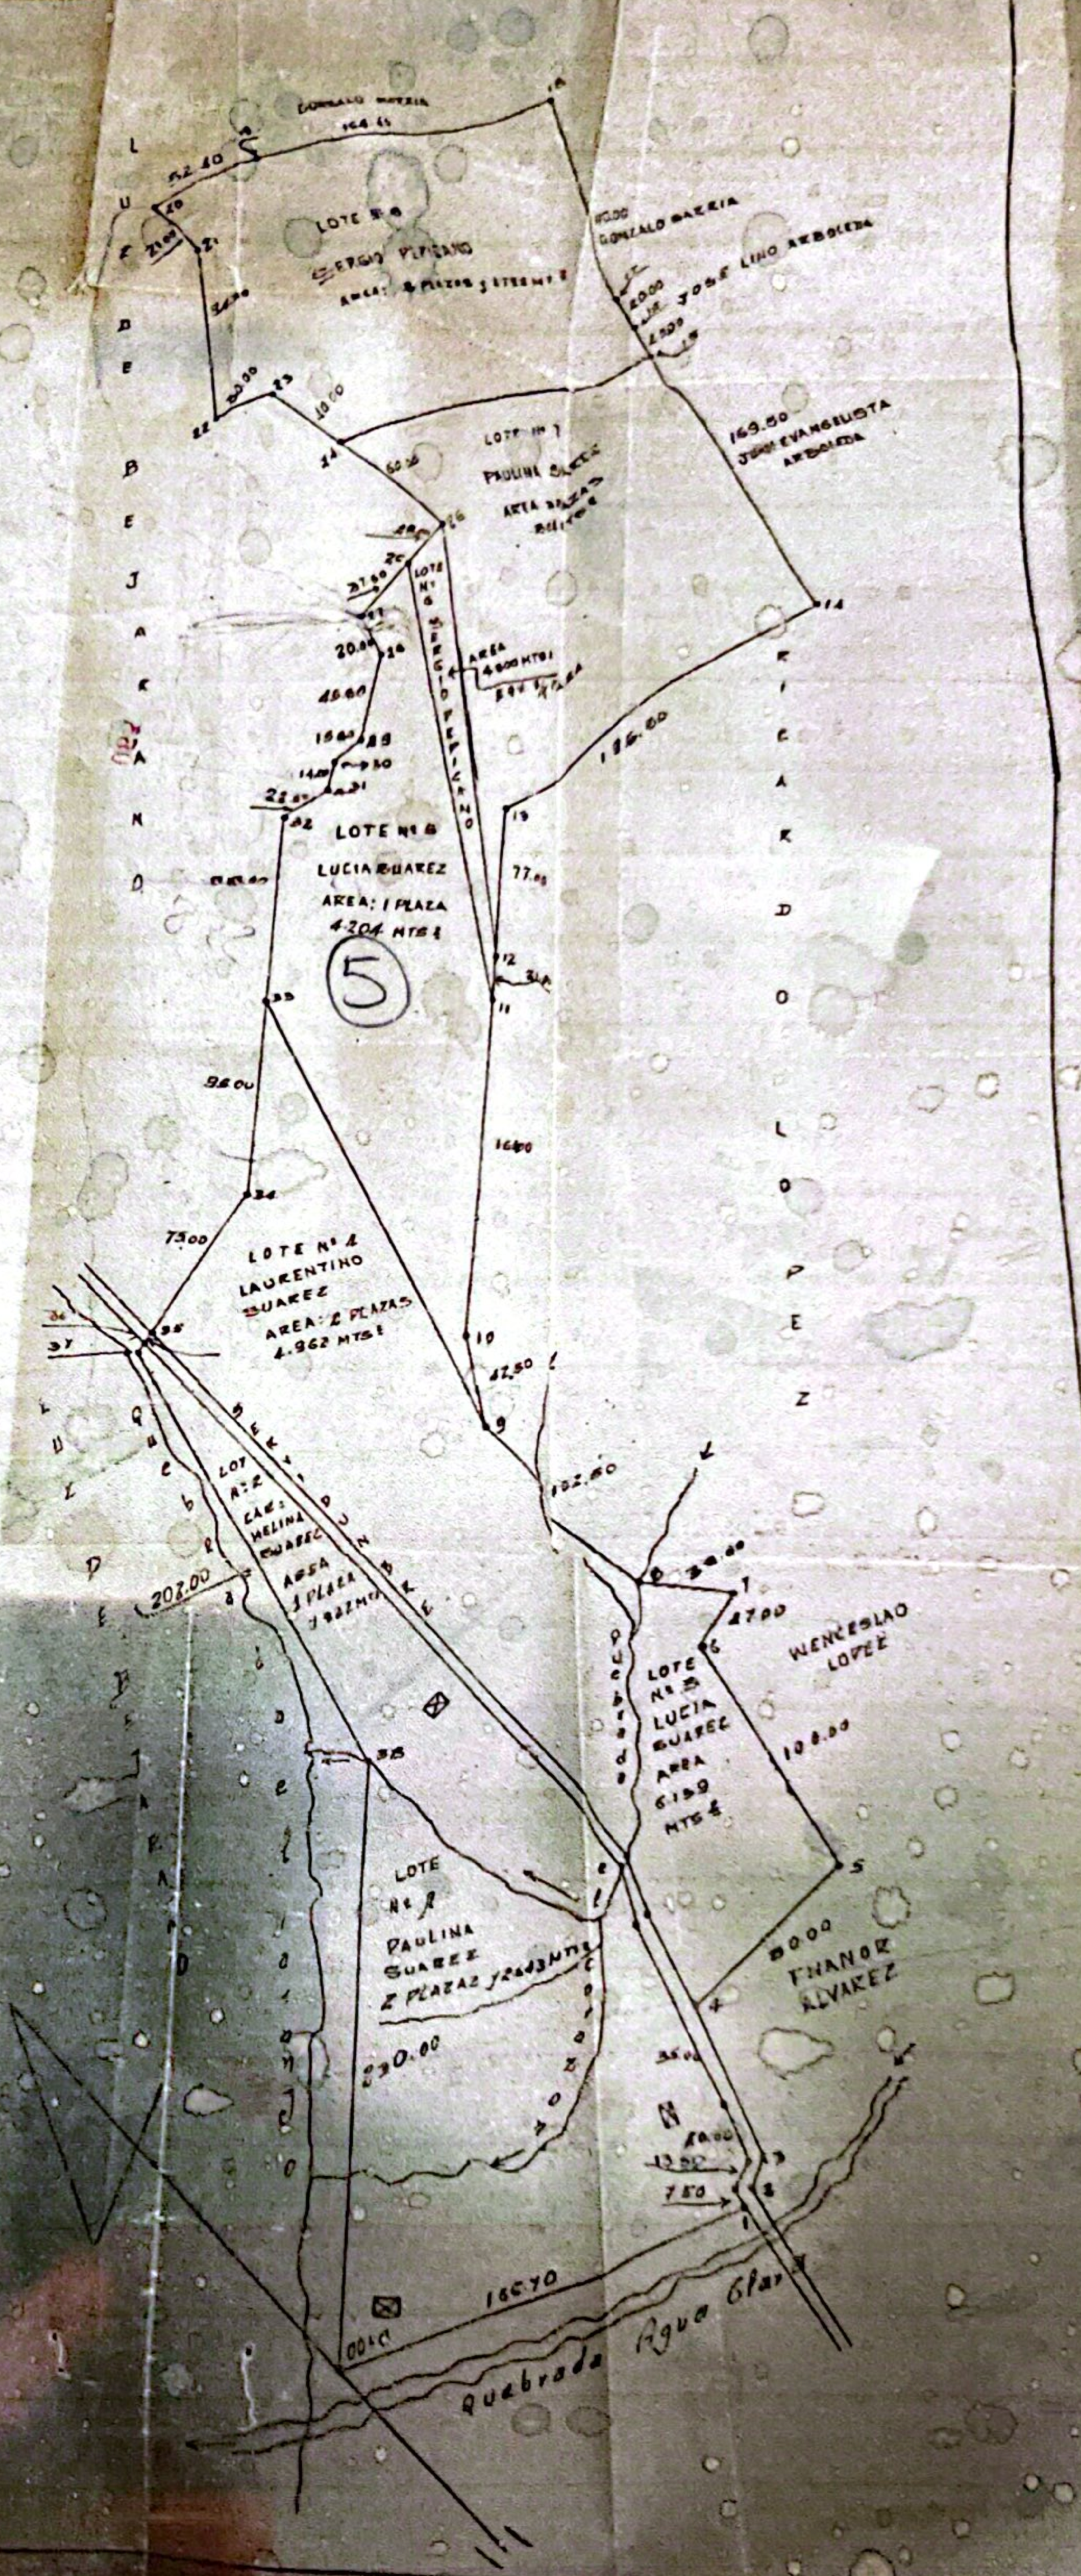

capturada en moto g⁸ plus
Oscar M.S Cedano
3 de noviembre de 2020 3:23 p. m.