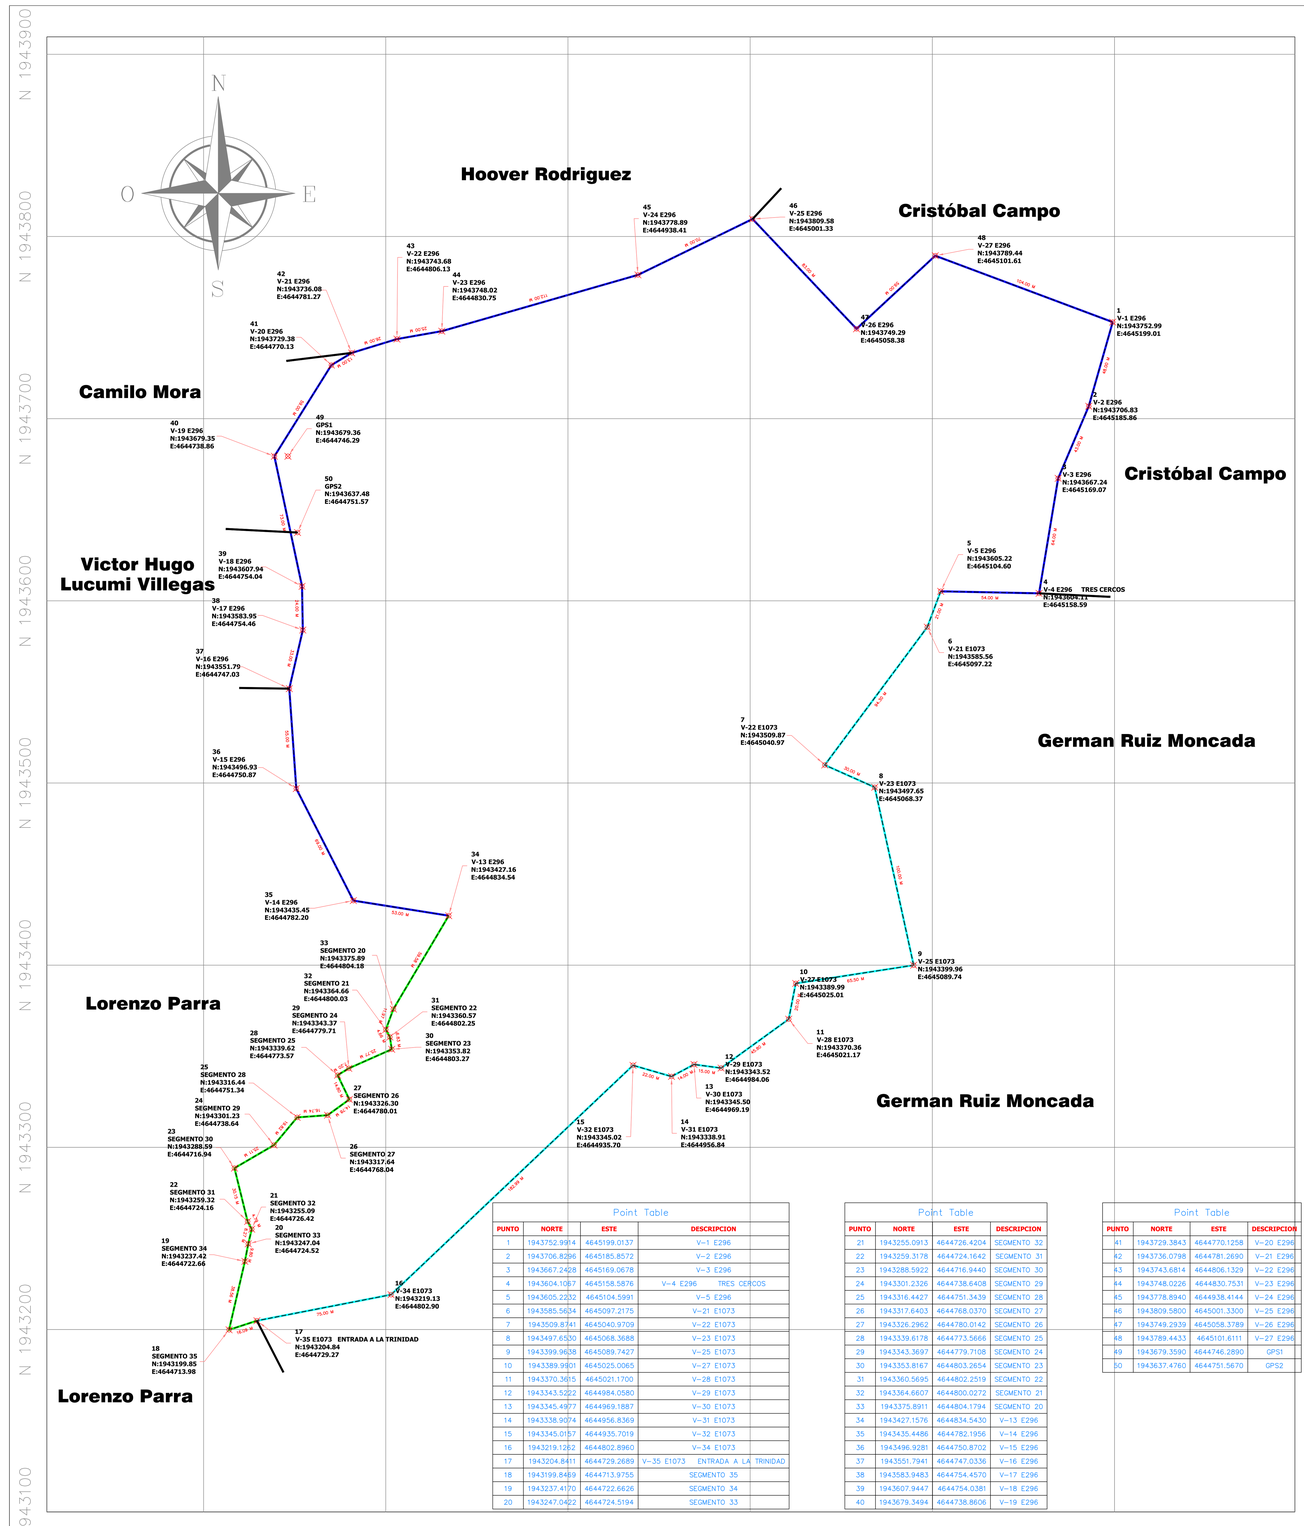


Point Table


PUNTO	NORTE	ESTE	DESCRIPCION
1	1943752.9914	4645199.0137	V-1 E296
2	1943706.8296	4645185.8572	V-2 E296
3	1943667.2408	4645169.0678	V-3 E296
4	1943604.1087	4645158.5876	V-4 E296 TRES CERCOS
5	1943605.2232	4645104.5991	V-5 E296
6	1943585.5634	4645097.2175	V-21 E1073
7	1943509.8741	4645040.9709	V-22 E1073
8	1943497.6520	4645068.3688	V-23 E1073
9	1943399.9638	4645089.7427	V-25 E1073
10	1943389.9901	4645025.0065	V-27 E1073
11	1943370.3615	4645021.1700	V-28 E1073
12	1943343.5222	4644984.0580	V-29 E1073
13	1943345.4977	4644969.1887	V-30 E1073
14	1943338.9074	4644956.8369	V-31 E1073
15	1943345.0157	4644935.7019	V-32 E1073
16	1943219.1262	4644802.8960	V-34 E1073
17	1943204.8411	4644729.2689	V-35 E1073 ENTRADA A LA TRINIDAD
18	1943199.8489	4644713.9755	SEGMENTO 35
19	1943237.4170	4644722.6626	SEGMENTO 34
20	1943247.0422	4644724.5194	SEGMENTO 33

Point Table

PUNTO	NORTE	ESTE	DESCRIPCION
21	1943255.0913	4644726.4204	SEGMENTO 32
22	1943259.3178	4644724.1642	SEGMENTO 31
23	1943288.5922	4644716.9440	SEGMENTO 30
24	1943301.2326	4644738.6408	SEGMENTO 29
25	1943316.4427	4644751.3439	SEGMENTO 28
26	1943317.6403	4644768.0370	SEGMENTO 27
27	1943326.2962	4644780.0142	SEGMENTO 26
28	1943339.6178	4644773.5666	SEGMENTO 25
29	1943343.3697	4644779.7108	SEGMENTO 24
30	1943353.8167	4644803.2654	SEGMENTO 23
31	1943360.5695	4644802.2519	SEGMENTO 22
32	1943364.6607	4644800.0272	SEGMENTO 21
33	1943375.8911	4644804.1794	SEGMENTO 20
34	1943427.1576	4644834.5430	V-13 E296
35	1943435.4486	4644782.1956	V-14 E296
36	1943496.9281	4644750.8702	V-15 E296
37	1943551.7941	4644747.0336	V-16 E296
38	1943583.9483	4644754.4570	V-17 E296
39	1943607.9447	4644754.0381	V-18 E296
40	1943679.3494	4644738.8606	V-19 E296

Point Table

PUNTO	NORTE	ESTE	DESCRIPCION
41	1943729.3843	4644770.1258	V-20 E296
42	1943736.0798	4644781.2690	V-21 E296
43	1943743.6814	4644806.1329	V-22 E296
44	1943748.0226	4644830.7531	V-23 E296
45	1943778.8940	4644938.4144	V-24 E296
46	1943809.5800	4645001.3300	V-25 E296
47	1943749.2939	4645058.3789	V-26 E296
48	1943789.4433	4645101.6111	V-27 E296
49	1943679.3590	4644746.2890	GPS1
50	1943637.4760	4644751.5670	GPS2

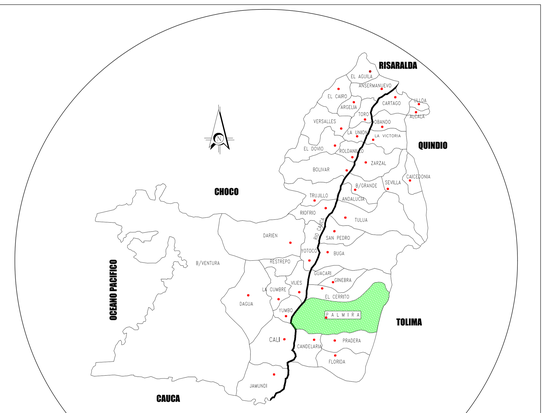

LOCALIZACION GENERAL
SIN ESCALA

COORDENADAS DE AMARRE

PUNTO	NORTE	ESTE	ELEVACION
GPS 01	1.943.679,3026 m	4.644.746,3911 m	1.503,9926 m
GPS 02	1.943.637,4128 m	4.644.751,6891 m	1.503,2711 m

Master Coordinate System
Coordinate System Name: MAGNA-SIRGAS_Origen-Nacional
Transformation Type: Classical 3D
Residual Distribution: None
Ellipsoid: GRS 1980
Projection Type: Transverse Mercator
Geoid Model: Geocol2004

CONVENCIONES

- Escritura 296
- Escritura 1073
- Quebrada
- Area total
- Gps

CUADRO DE AREAS

AREA ESCRITURA NO# 296: 25 PL. 2156 M2

OBSERVACIONES

Los nodos denominados al final con sufijo (E296) quiere decir que pertenecen a la escritura 296.

Los nodos denominados al final con sufijo (E1073) quiere decir que pertenecen a la escritura 1073.

LEVANTAMIENTO TOPOGRAFICO
PREDIO AYACUCHO LA TRINIDAD
CORREGIMIENTO LA BUITRERA
MUNICIPIO DE PALMIRA
DEPARTAMENTO DEL VALLE DEL CAUCA

PROPIETARIO: ROSA EUGENIA SAAVEDRA ARCINIEGAS

LEVANTO: TOP. CRISTIAN DANIEL
TP:01-16531 CPNT

FECHA: 13 OCTUBRE 2026

REGISTRO DIGITAL

ESCALA: 1_1000 **PLANO N°:** 1 DE 1