


ESCRITURA 296

ESCRITURA 1073

ESCRITURA 196

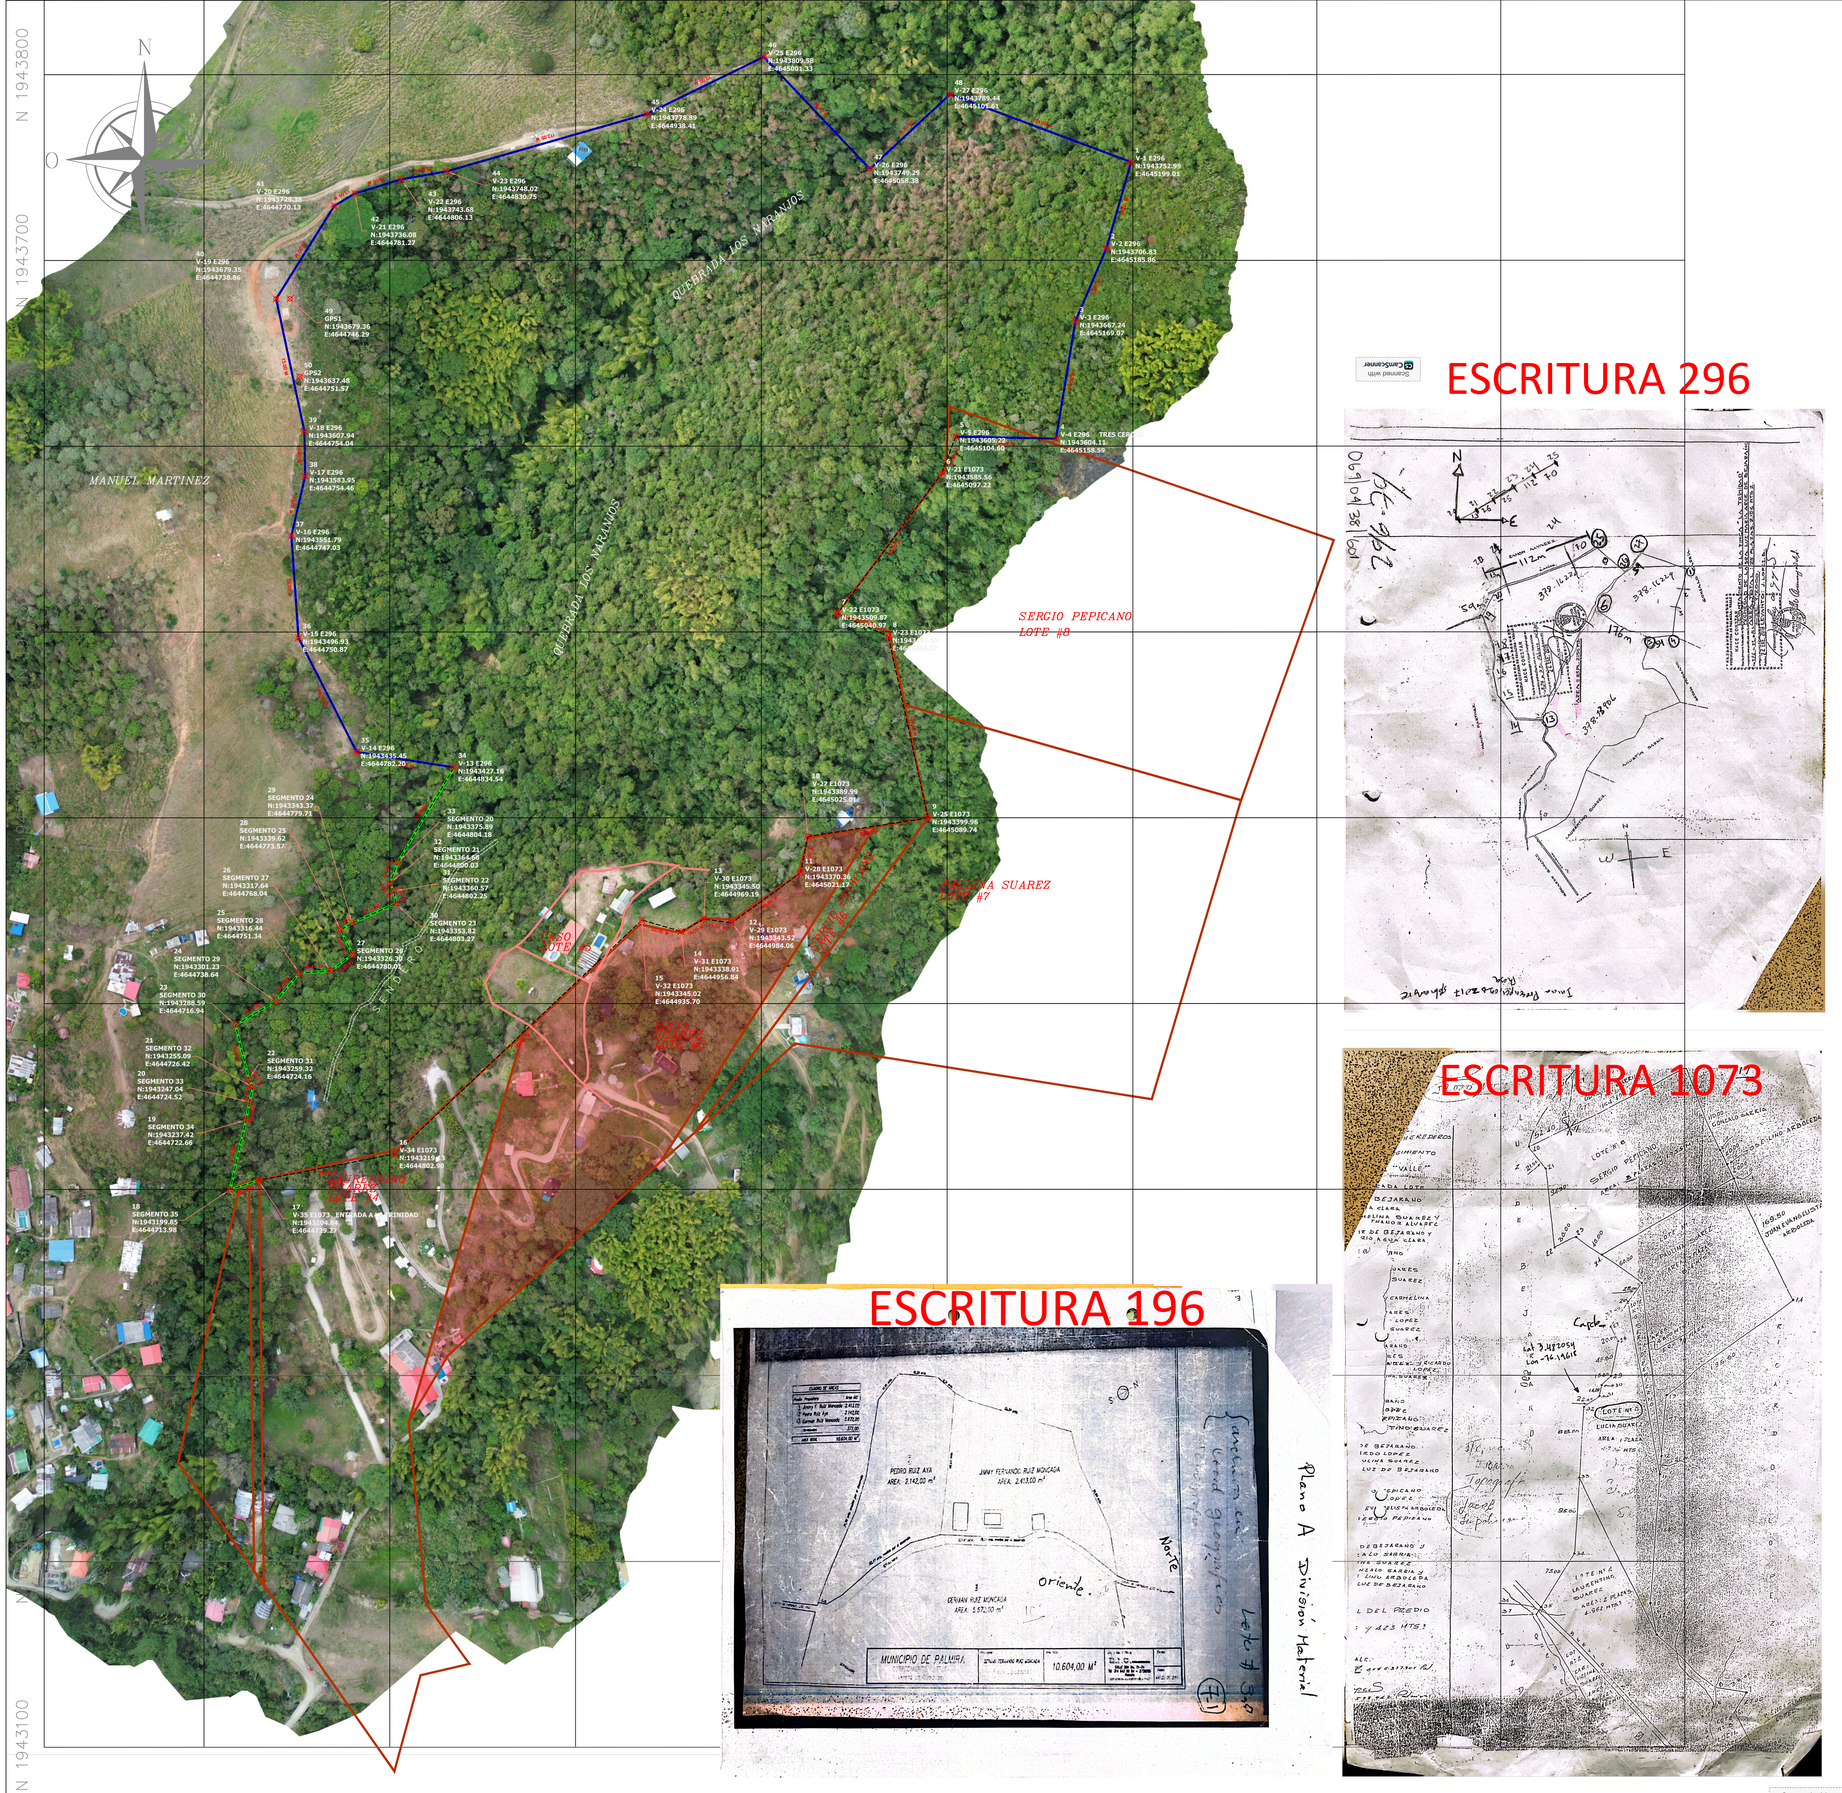

LOCALIZACION GENERAL
SIN ESCALA

COORDENADAS DE AMARRE

PUNTO	NORTE	ESTE	ELEVACION
GPS 01	1.943.679,3026 m	4.644.746,3911 m	1.503,9926 m
GPS 02	1.943.637,4128 m	4.644.751,6891 m	1.503,2711 m

Master Coordinate System
Coordinate System Name: MAGNA-SIRGAS_Origen-Nacional
Transformation Type: Classical 3D
Residual Distribution: None
Ellipsoid: GRS 1980
Projection Type: Transverse Mercator
Geoid Model: Geocol2004

CONVENCIONES

- Escritura 296
- Escritura 1073
- Escritura 196
- Quebrada
- Area total
- Gps

CUADRO DE AREAS

AREA ESCRITURA NO# 296: 25 PL. 2156 M2

OBSERVACIONES

La información documental y cartográfica contenida en la Escritura Pública No. 1073 permite reconstruir e identificar el lindero común entre Casa del Sol y La Trinidad. Sin embargo, la determinación del área total de Casa del Sol requiere información topográfica complementaria del interior del predio, al cual no se tuvo acceso para la elaboración del presente estudio. En consecuencia, dicha área no constituye una determinación técnica de este informe.

LEVANTAMIENTO TOPOGRAFICO
PREDIO AYACUCHO LA TRINIDAD
CORREGIMIENTO LA BUITRERA
MUNICIPIO DE PALMIRA
DEPARTAMENTO DEL VALLE DEL CAUCA

PROPIETARIO: ROSA EUGENIA SAAVEDRA ARCINIEGAS

LEVANTO: TOP. CRISTIAN DANIEL
TP:01-16531 CPNT

FECHA: 13 OCTUBRE 2026

REGISTRO DIGITAL

ESCALA: 1_1000 **PLANO N°:** 1 DE 1

Scanned with CamScanner