
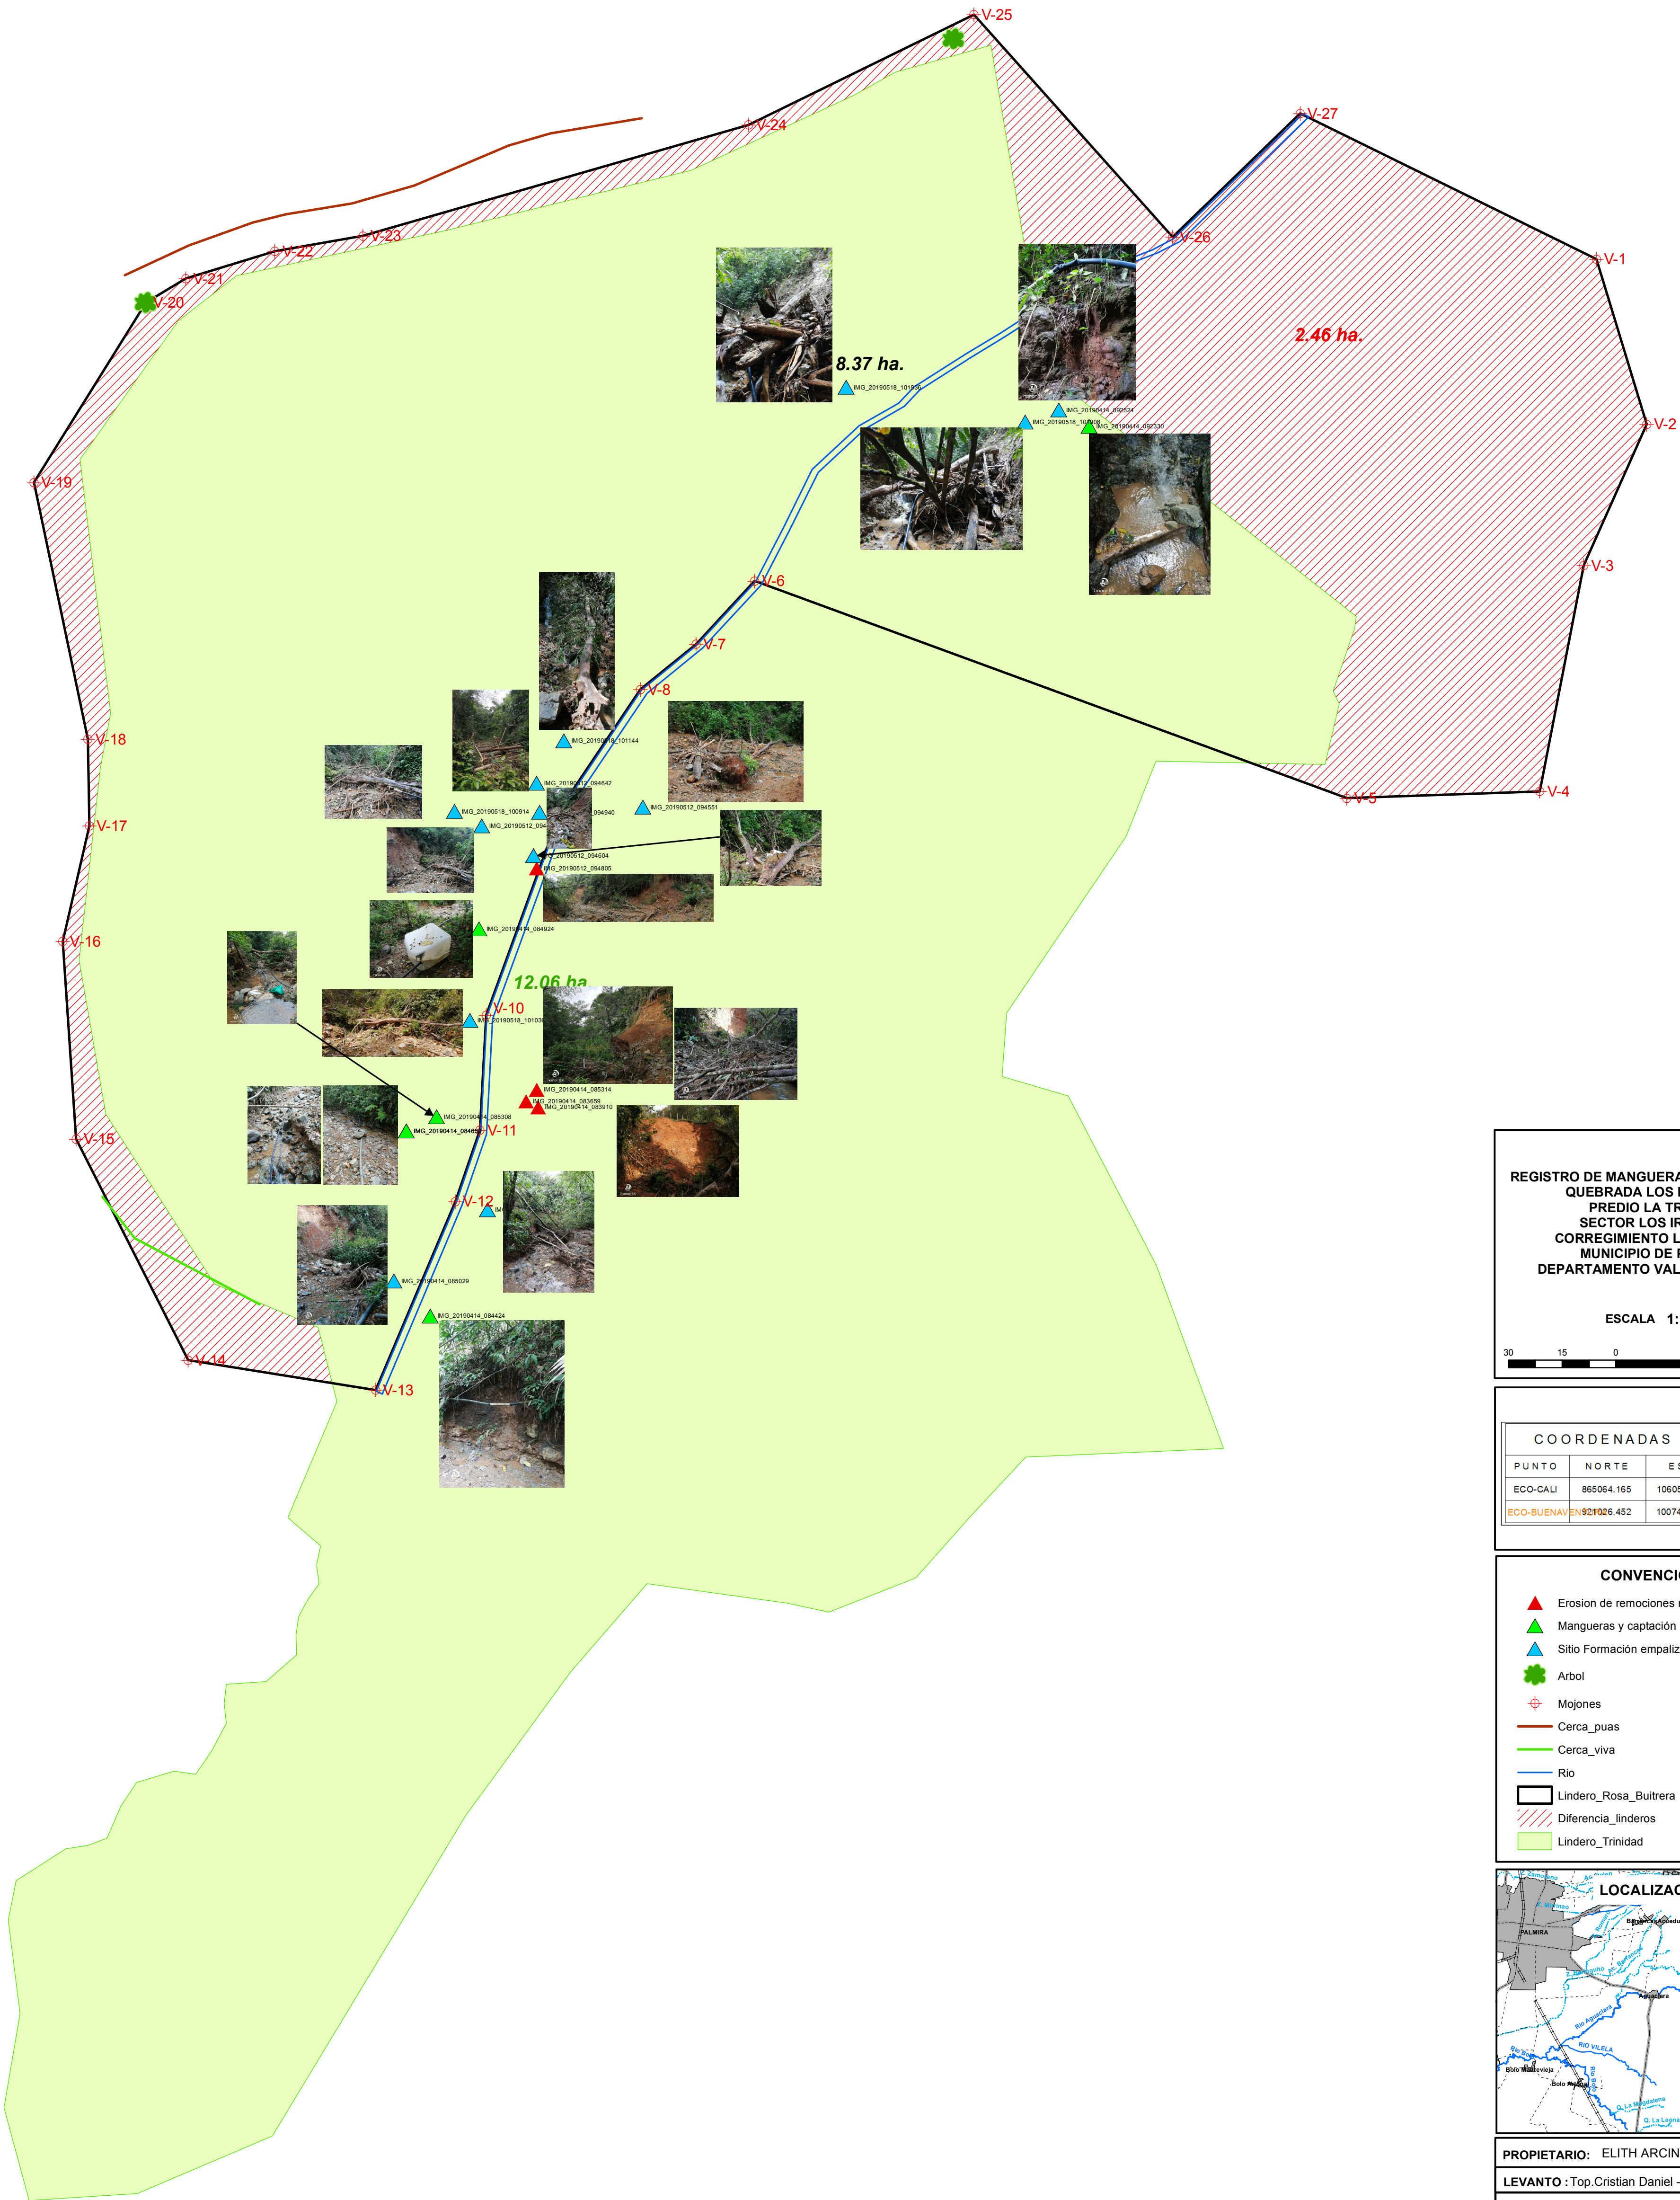


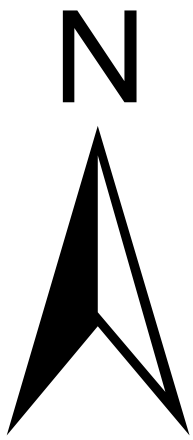

REGISTRO DE MANGUERAS EN MAL ESTADO
QUEBRADA LOS NARANJOS
PREDIO LA TRINIDAD
SECTOR LOS IRACALES
CORREGIMIENTO LA BUITRERA
MUNICIPIO DE PALMIRA
DEPARTAMENTO VALLE DEL CAUCA

ESCALA 1:1,000

30

15

0

30 Meters

COORDENADAS DE AMARRE			
PUNTO	NORTE	ESTE	ELEVACION
ECO-CALI	865064.165	1060559.211	1027.496
ECO-BUENAVEN	821026.452	1007451.177	57.711

CONVENCIONES

- Erosion de remociones masivas
- Mangueras y captación
- Sitio Formación empalizada
- Arbol
- Mojones
- Cerca_puas
- Cerca_viva
- Rio
- Lindero_Rosa_Buitrera
- Diferencia_linderos
- Lindero_Trinidad

LOCALIZACION

PROPIETARIO: ELITH ARCINIEGAS DE SAAVEDRA

LEVANTO: Top.Cristian Daniel - TP:01-16531-CPNT

REGISTRO FOTOGRAFICO : Diego F. Sandoval

REVISION : Carlos Alberto Chalarca

FECHA : Marzo 2019

ARCHIVO :
C:\Mis Documentos\Planos\Haciendas_Varias\Rosa_Buitrera\Mapas\Rosa_Buitrera_medio_plego.mxd