
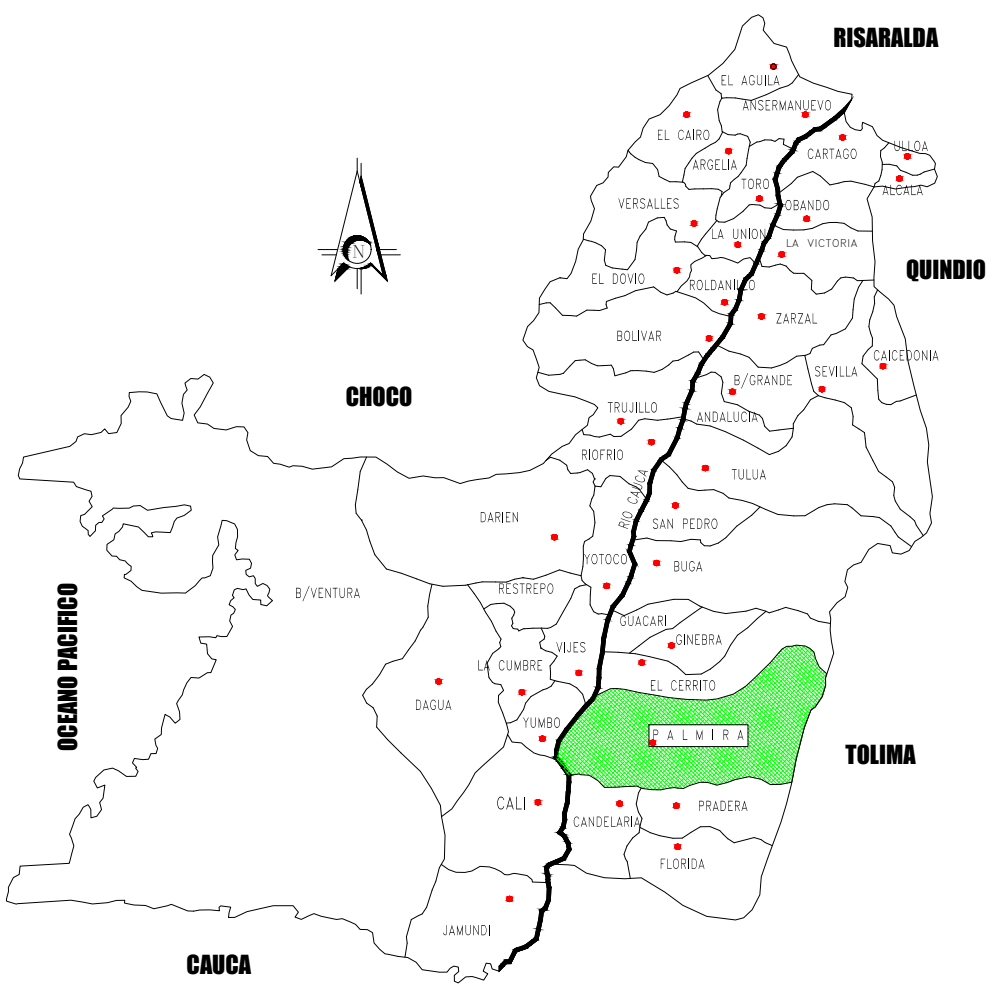


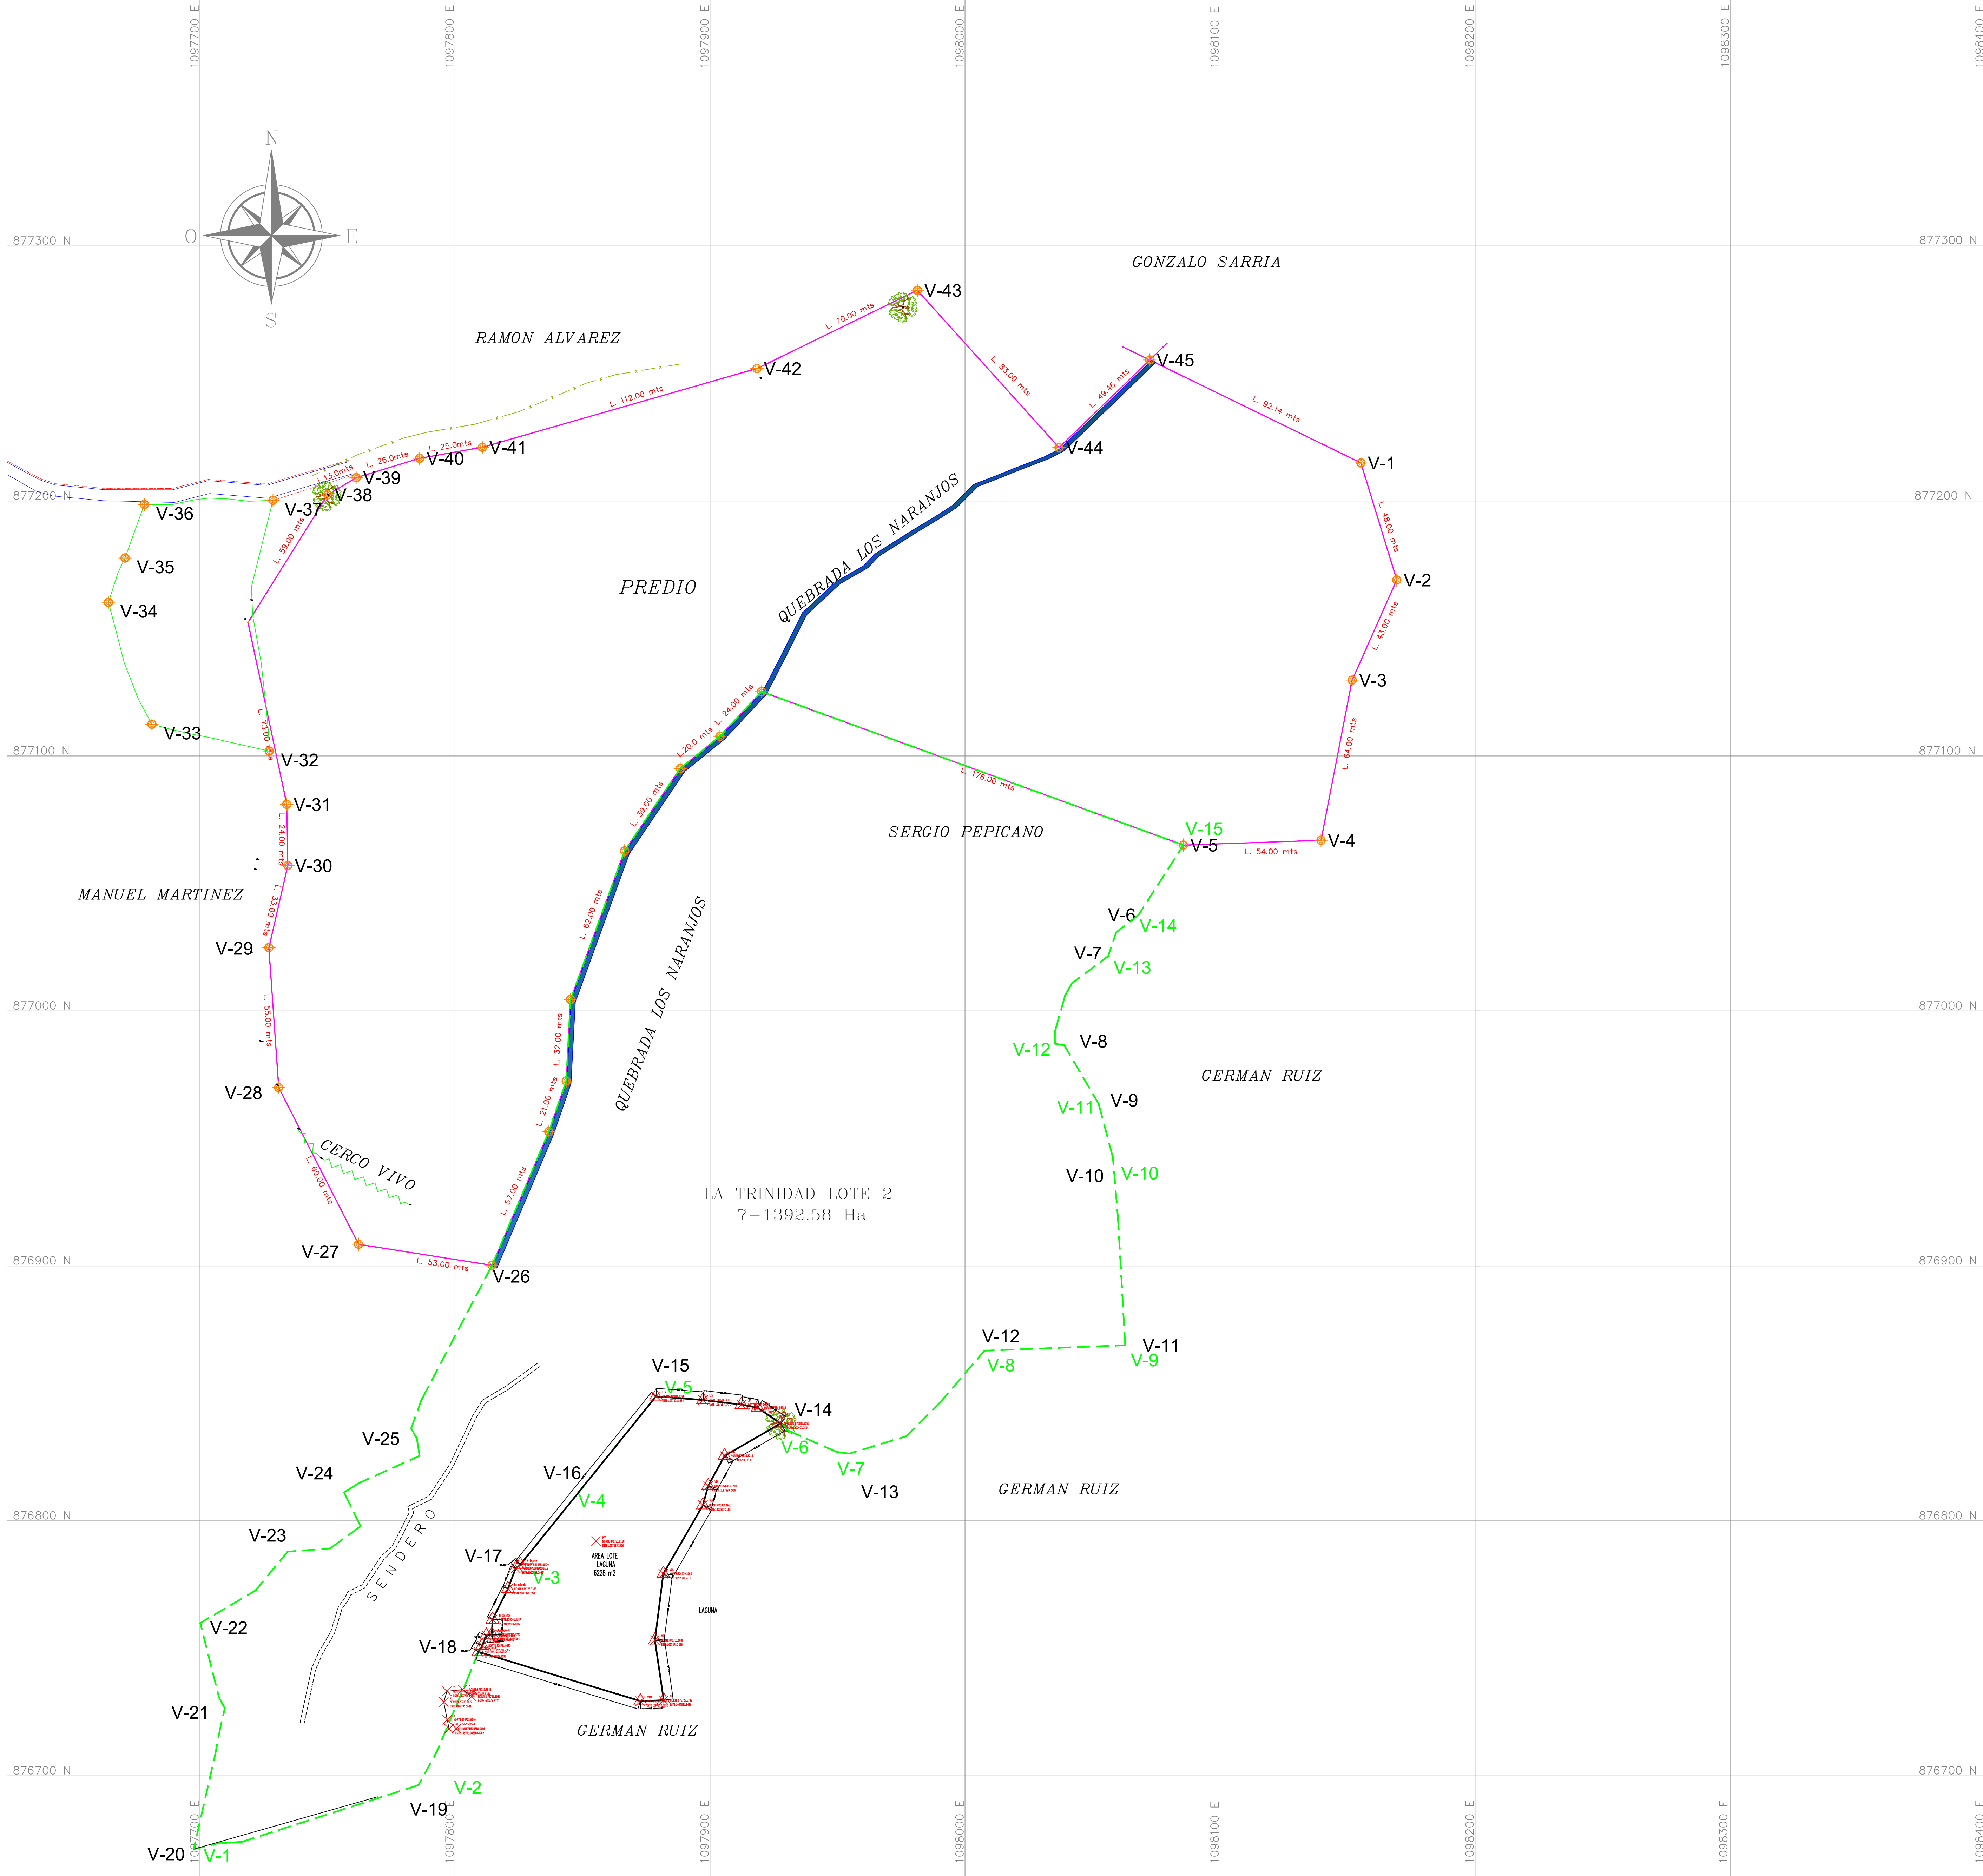

LOCALIZACION GENERAL
SIN ESCALA

COORDENADAS DE AMARRE			
PUNTO	NORTE	ESTE	ELEVACION
ECO-CALI	865064.165	1060559.211	1027.496
ECO-BUENAVENTURA	921026.452	1007451.177	57.711

CONVENCIONES

ARBOL	
VERTICES LINDERO	
VIA	
AREA PREDIO	
CERCO ALAMBRE PUAS	
CERCO VIVO	
RIO O QUEBRADA	

CUADRO DE AREA TRINIDAD

8 Ha 3700 m2

CUADRO DE AREA TRINIDAD 2

7 Ha 0619 m2

CUADRO DE AREA LOTE LAGUNA

0 Ha 6228 m2

LEVANTAMIENTO TOPOGRAFICO
PREDIO TRINIDAD Y TRINIDAD 2
CORREGIMIENTO LA BUITRERA
MUNICIPIO DE PALMIRA
DEPARTAMENTO DEL VALLE DEL CAUCA

PROPIETARIO: LUZ MARINA ARCE DE BEJARANO

LEVANTO: TOP. CRISTIAN DANIEL
TP: CPNT

FECHA: MARZO 2019

REGISTRO DIGITAL

ESCALA: 1_750 PLANO N°: 1 DE 1